



【参考】ゲート寸法

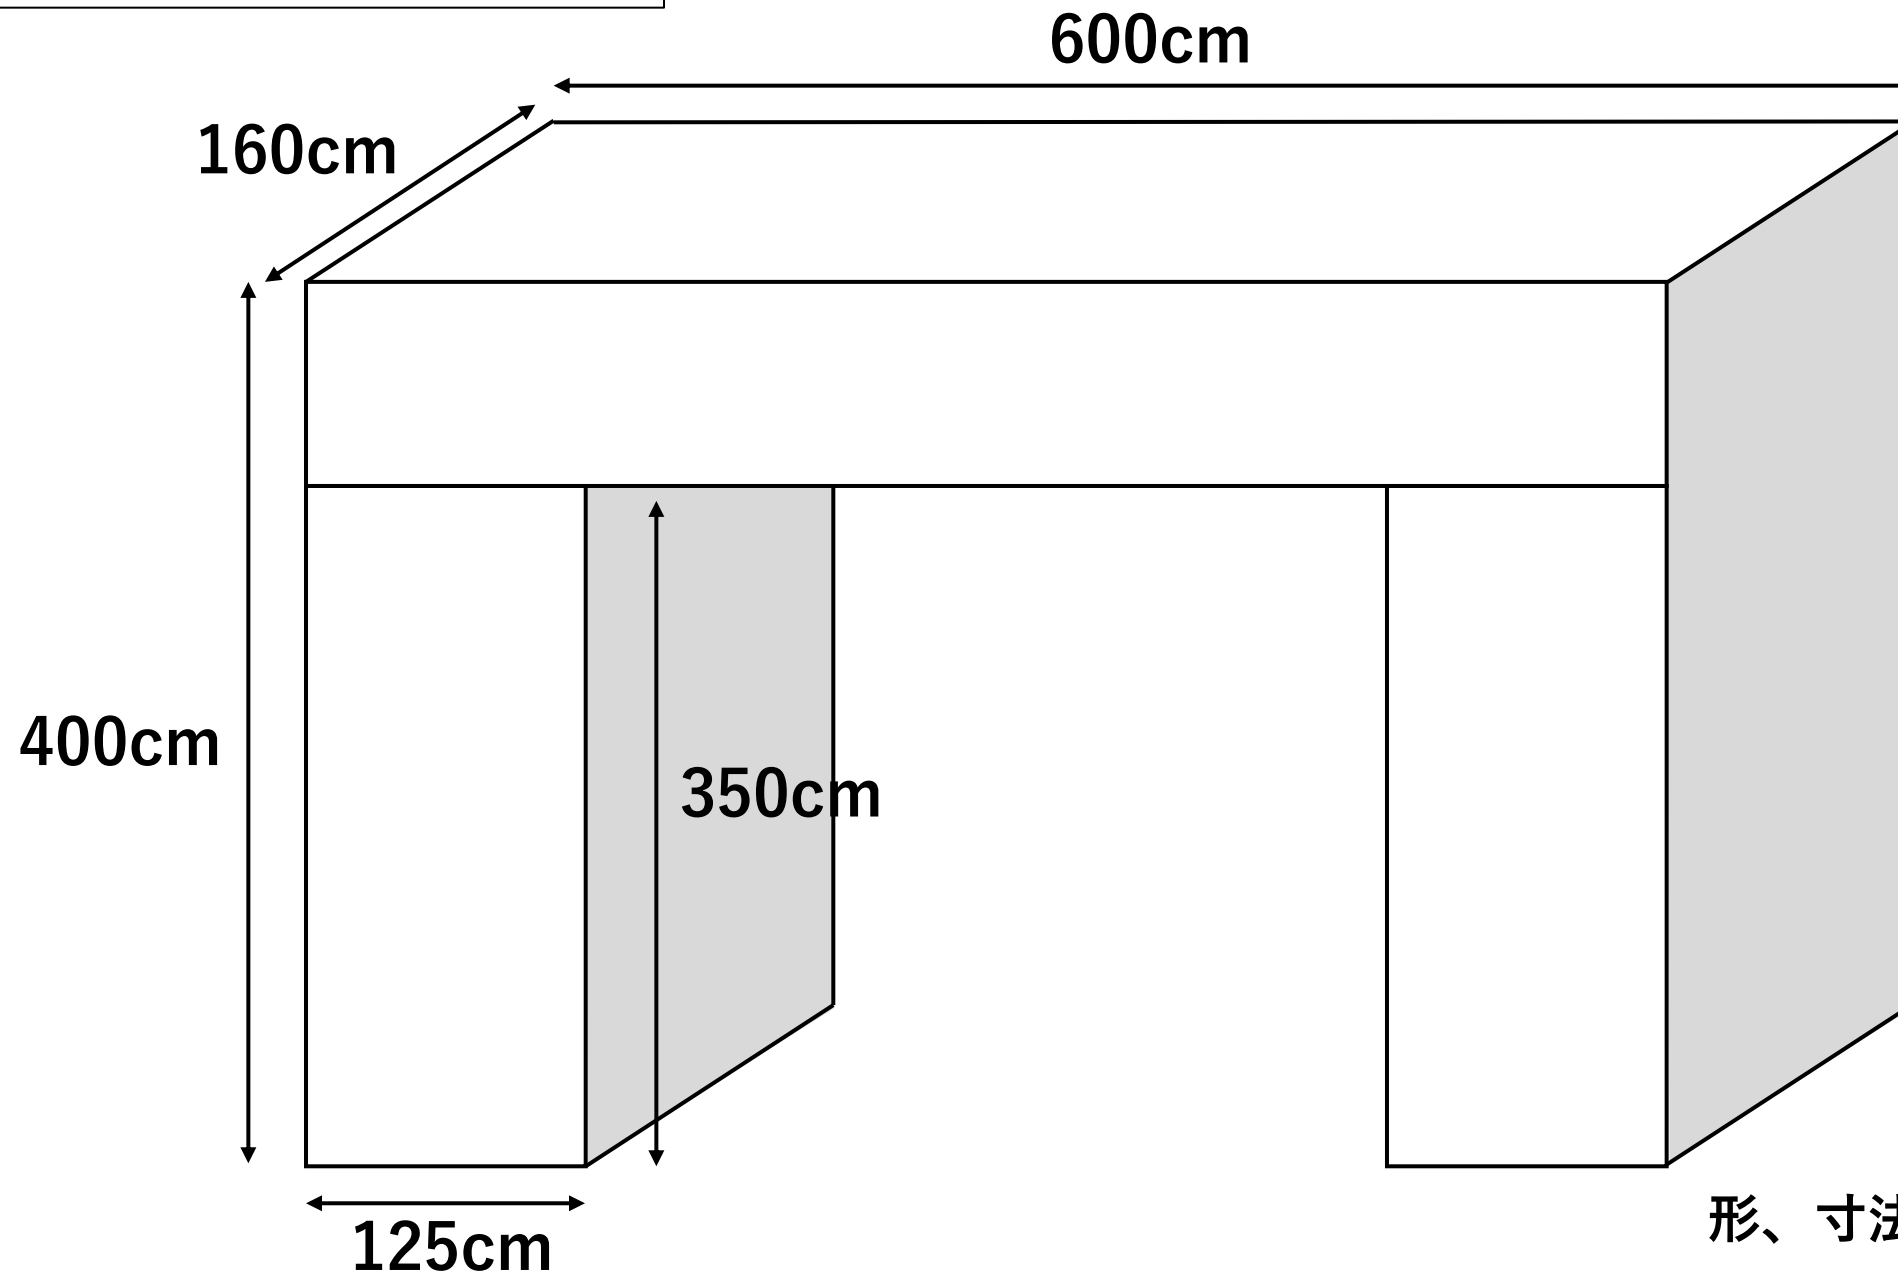

左右対称
形、寸法はあくまでも予定

【参考】看板寸法

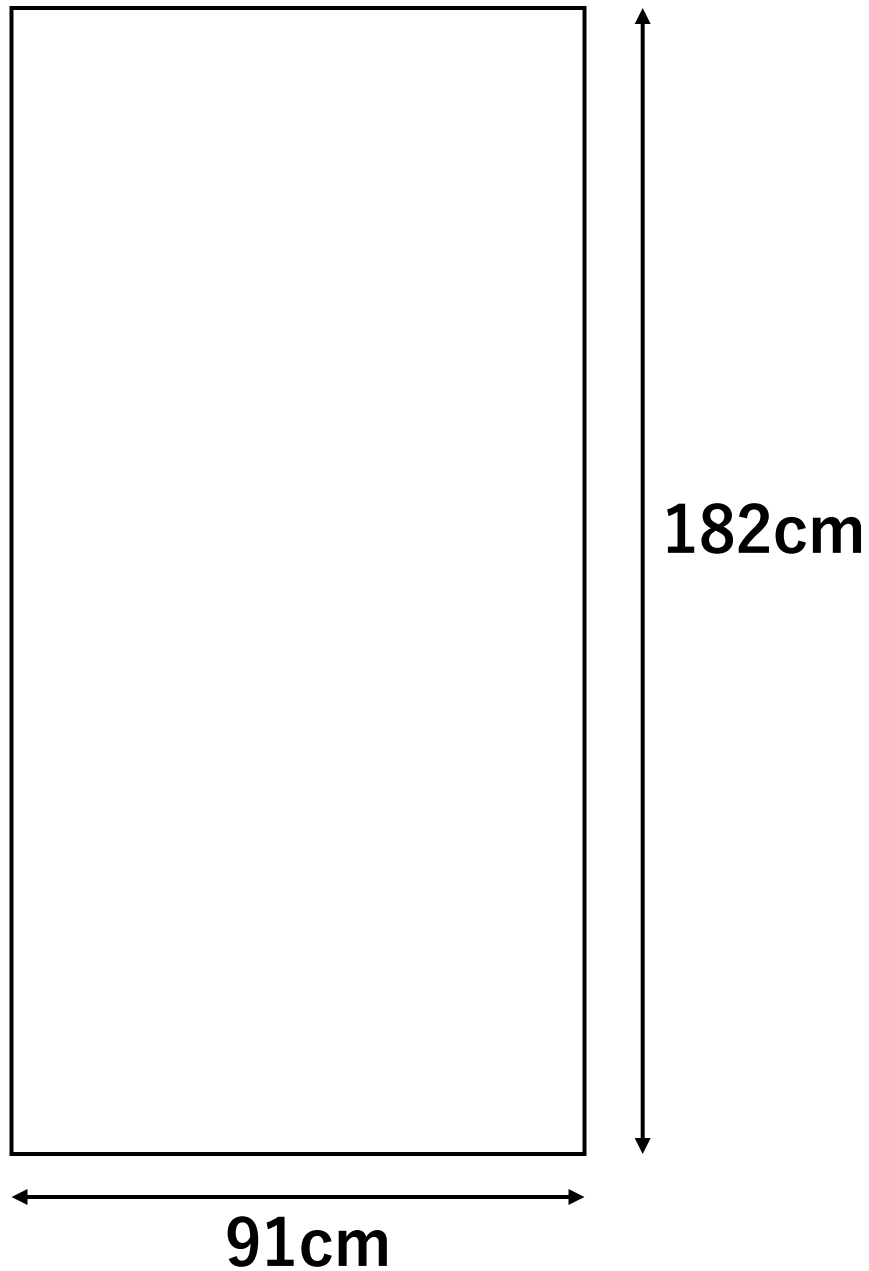

形、寸法はあくまでも予定
大きく変わる可能性がある